DOSSIER PLANS - PROJET FICTIF DE TEST

TOUR HORIZON

Résidence grand standing R+40 - Dakar

RDC	Hall, loge gardien, logement gardien, 2 commerces, lobby, syndic
R+1 à R+2	Sport, spa, coworking, cinéma, salle polyvalente, enfants
R+3 à R+35	Étage courant : 2 x F5 (276 m²) + 2 x F2 (67,5 m²)
R+36 à R+39	Étage type 2 : F5 + F4 + F2 + 2 studios
R+40	Penthouse : suite master, réception, cuisine pro, home cinéma
Annexe	Corrigé : surfaces + métré cloisons (à masquer pour le test)

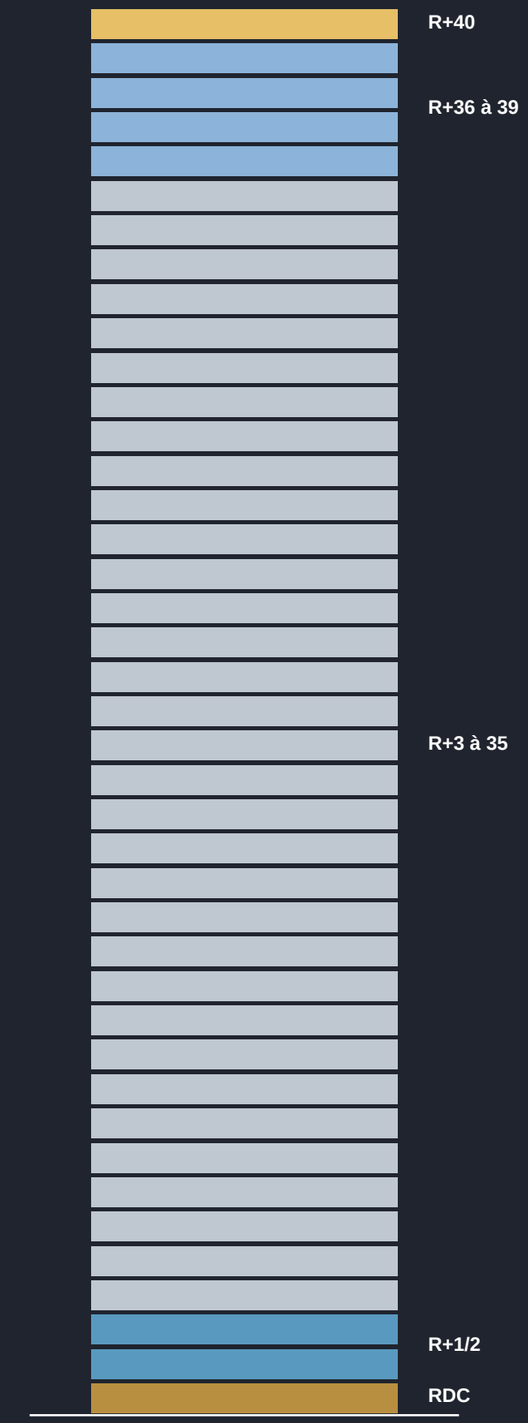

Emprise 32 x 24 m - 41 niveaux - 6 planches - 29/10/2026

Document généré pour test d'IA de métré. Ne pas utiliser pour exécution.

PLAN TEST - PROJET FICTIF

TOUR HORIZON R+40

Résidence grand standing - Dakar

Emprise 32,00 x 24,00 m

RDC

Rez-de-chaussée - Accueil, loge, commerces

Niveaux concernés	**1**
Hauteur cloisons (dalle/plafond)	**4.00 m**
Échelle	**1/125 (format A3)**
Date	**29/10/2026**
Planche	**2/6**

0 m — 5 m

LÉGENDE

- Voile / mur béton 20 cm
- Cloison 72/48 - 1 BA13 std chaque face
- Cloison 72/48 - BA13 hydro H1 (pièces humides)
- Cloison 98/48 - 2 BA13 chaque face + laine 45 mm
- Limite de zone (sans cloison)

NOTES

- Cotes en mètres, nu intérieur fini.
- Étiquette : code / pièce / dimensions / surface.
- Ouvertures (portes) non représentées.
- Cloisons BA13 = repérage couleur.
- Pièces humides : plaques hydro H1.
- Plan fictif destiné aux tests IA.

UniC Plaquiste - Dakar

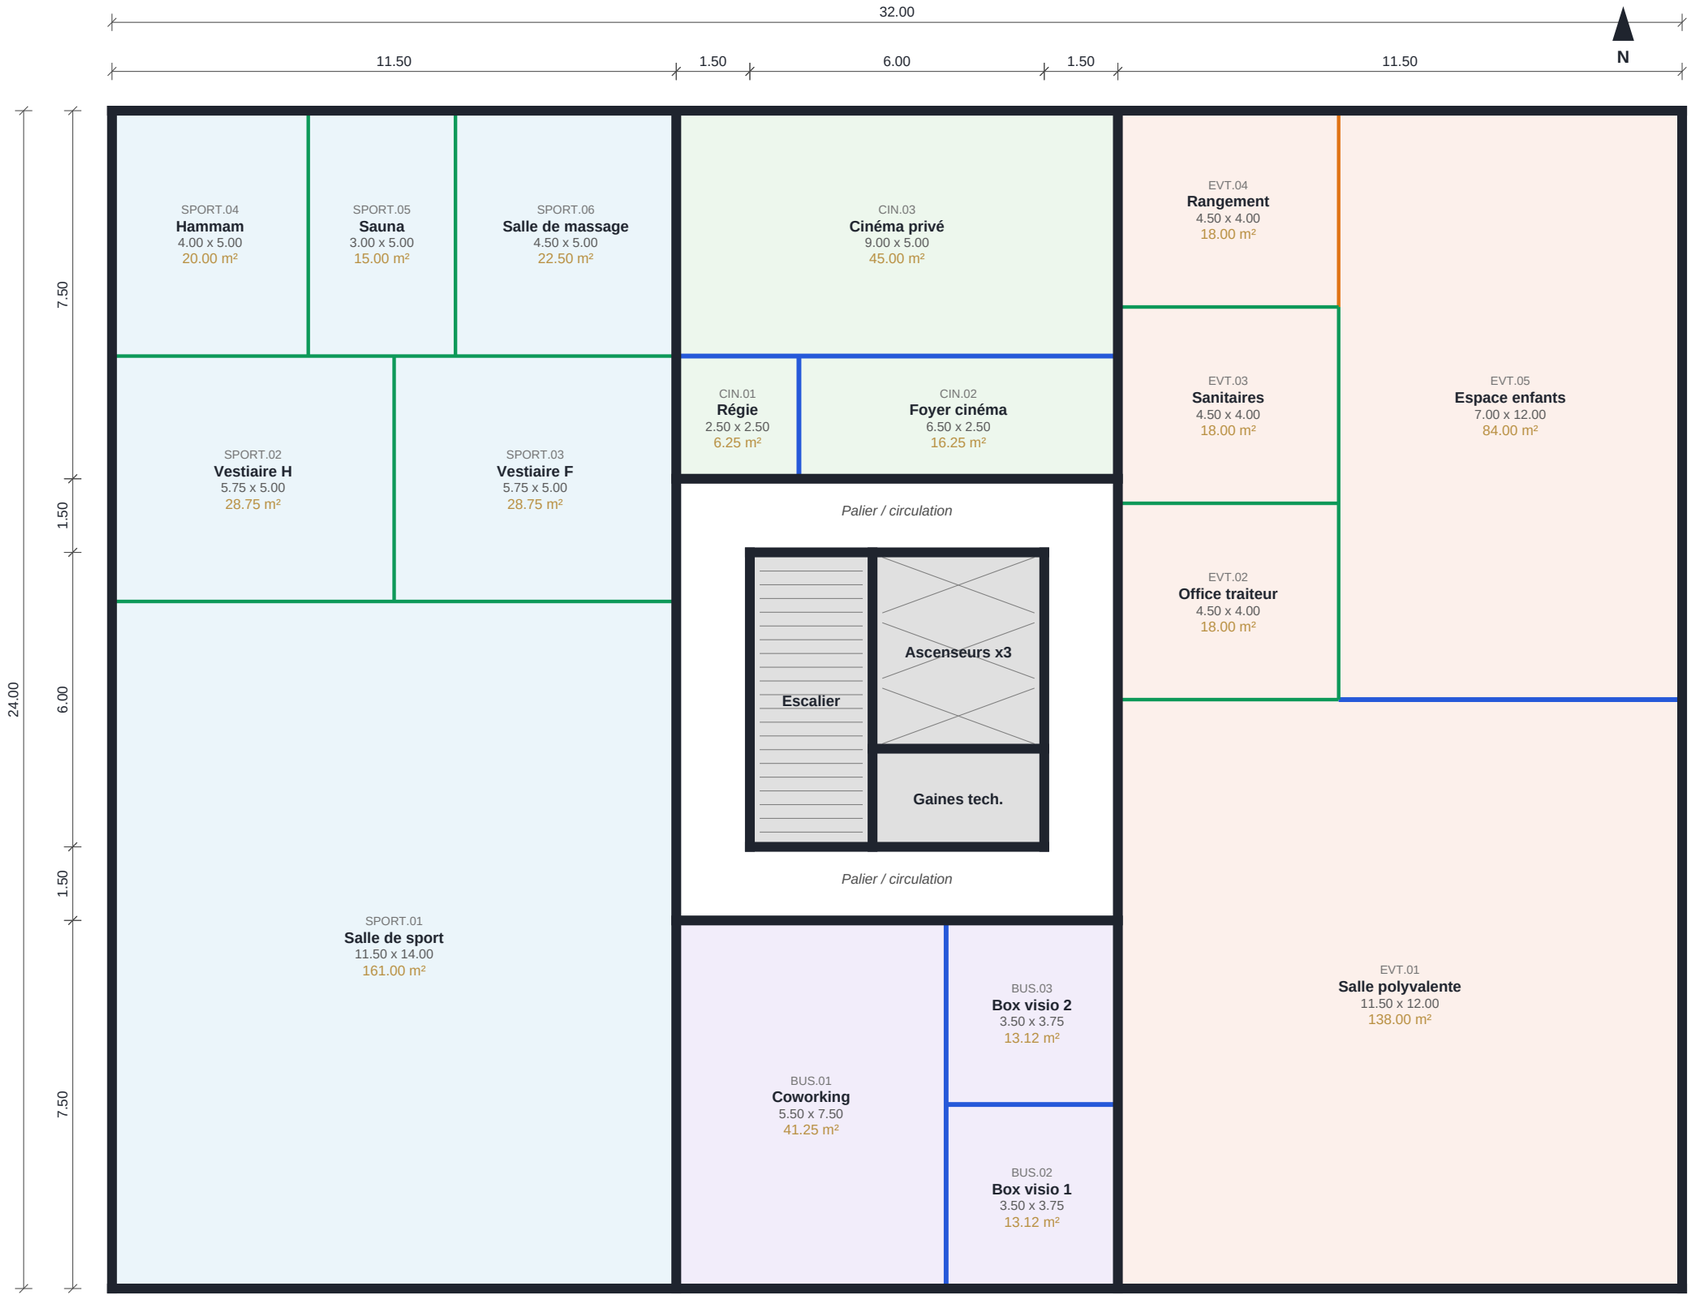

PLAN TEST - PROJET FICTIF

TOUR HORIZON R+40

Résidence grand standing - Dakar

Emprise 32,00 x 24,00 m

R+1 et R+2

Équipements communs résidents

Niveaux concernés	**2**
Hauteur cloisons (dalle/plafond)	**3.50 m**
Échelle	**1/125 (format A3)**
Date	**29/10/2026**
Planche	**3/6**

0 m — 5 m

LÉGENDE

- Voile / mur béton 20 cm
- Cloison 72/48 - 1 BA13 std chaque face
- Cloison 72/48 - BA13 hydro H1 (pièces humides)
- Cloison 98/48 - 2 BA13 chaque face + laine 45 mm
- Limite de zone (sans cloison)

NOTES

- Cotes en mètres, nu intérieur fini.
- Étiquette : code / pièce / dimensions / surface.
- Ouvertures (portes) non représentées.
- Cloisons BA13 = repérage couleur.
- Pièces humides : plaques hydro H1.
- Plan fictif destiné aux tests IA.

UniC Plaquiste - Dakar

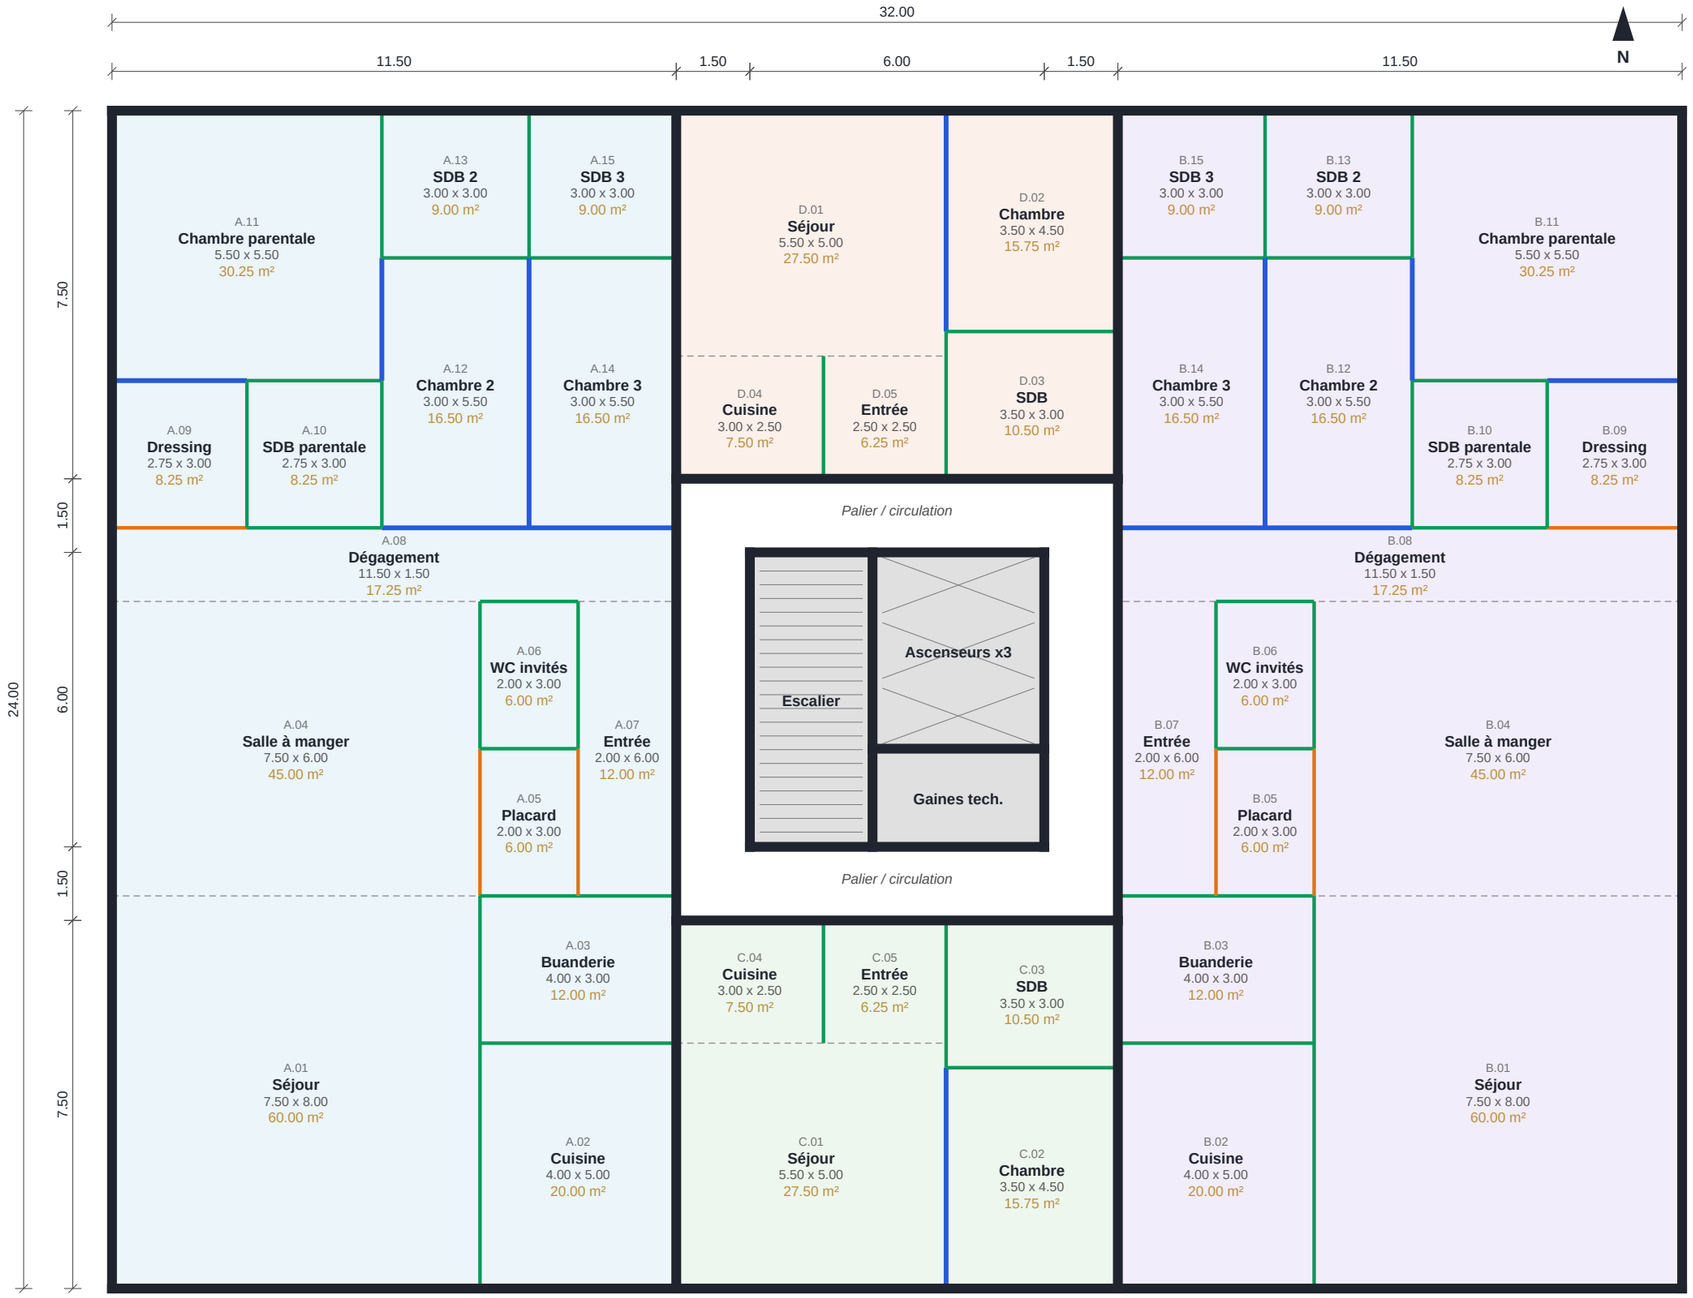

PLAN TEST - PROJET FICTIF

TOUR HORIZON R+40

Résidence grand standing - Dakar

Emprise 32,00 x 24,00 m

R+3 à R+35

Étage courant type 1 - 2 x F5 + 2 x F2

Niveaux concernés	**33**
Hauteur cloisons (dalle/plafond)	**2.80 m**
Échelle	**1/125 (format A3)**
Date	**29/10/2026**
Planche	**4/6**

0 m — 5 m

LÉGENDE

- Voile / mur béton 20 cm
- Cloison 72/48 - 1 BA13 std chaque face
- Cloison 72/48 - BA13 hydro H1 (pièces humides)
- Cloison 98/48 - 2 BA13 chaque face + laine 45 mm
- Limite de zone (sans cloison)

NOTES

- Cotes en mètres, nu intérieur fini.
- Étiquette : code / pièce / dimensions / surface.
- Ouvertures (portes) non représentées.
- Cloisons BA13 = repérage couleur.
- Pièces humides : plaques hydro H1.
- Plan fictif destiné aux tests IA.

UniC Plaquiste - Dakar

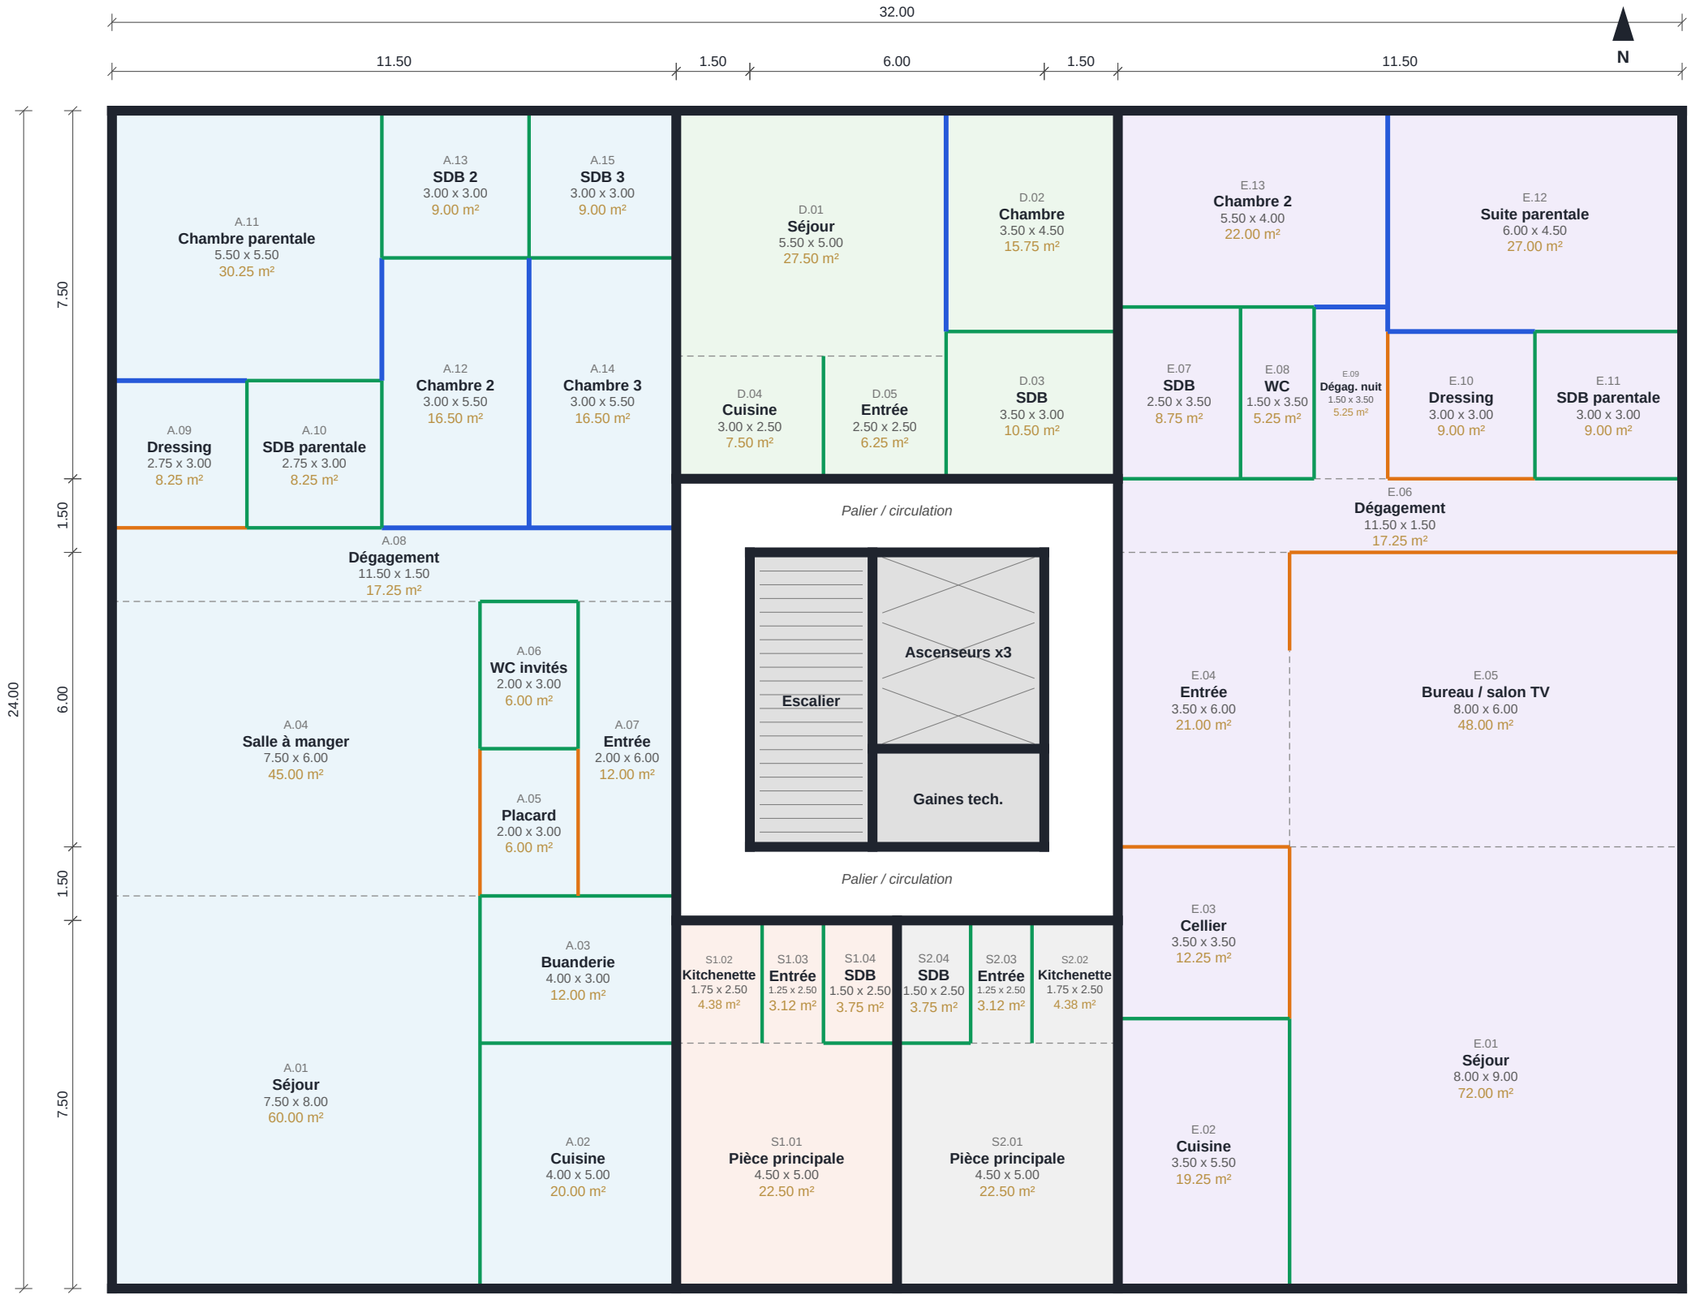

PLAN TEST - PROJET FICTIF

TOUR HORIZON R+40

Résidence grand standing - Dakar

Emprise 32,00 x 24,00 m

R+36 à R+39

Étage type 2 - F5 + F4 + F2 + 2 studios

Niveaux concernés	**4**
Hauteur cloisons (dalle/plafond)	**2.80 m**
Échelle	**1/125 (format A3)**
Date	**29/10/2026**
Planche	**5/6**

0 m — 5 m

LÉGENDE

- Voile / mur béton 20 cm
- Cloison 72/48 - 1 BA13 std chaque face
- Cloison 72/48 - BA13 hydro H1 (pièces humides)
- Cloison 98/48 - 2 BA13 chaque face + laine 45 mm
- Limite de zone (sans cloison)

NOTES

- Cotes en mètres, nu intérieur fini.
- Étiquette : code / pièce / dimensions / surface.
- Ouvertures (portes) non représentées.
- Cloisons BA13 = repérage couleur.
- Pièces humides : plaques hydro H1.
- Plan fictif destiné aux tests IA.

UniC Plaquiste - Dakar

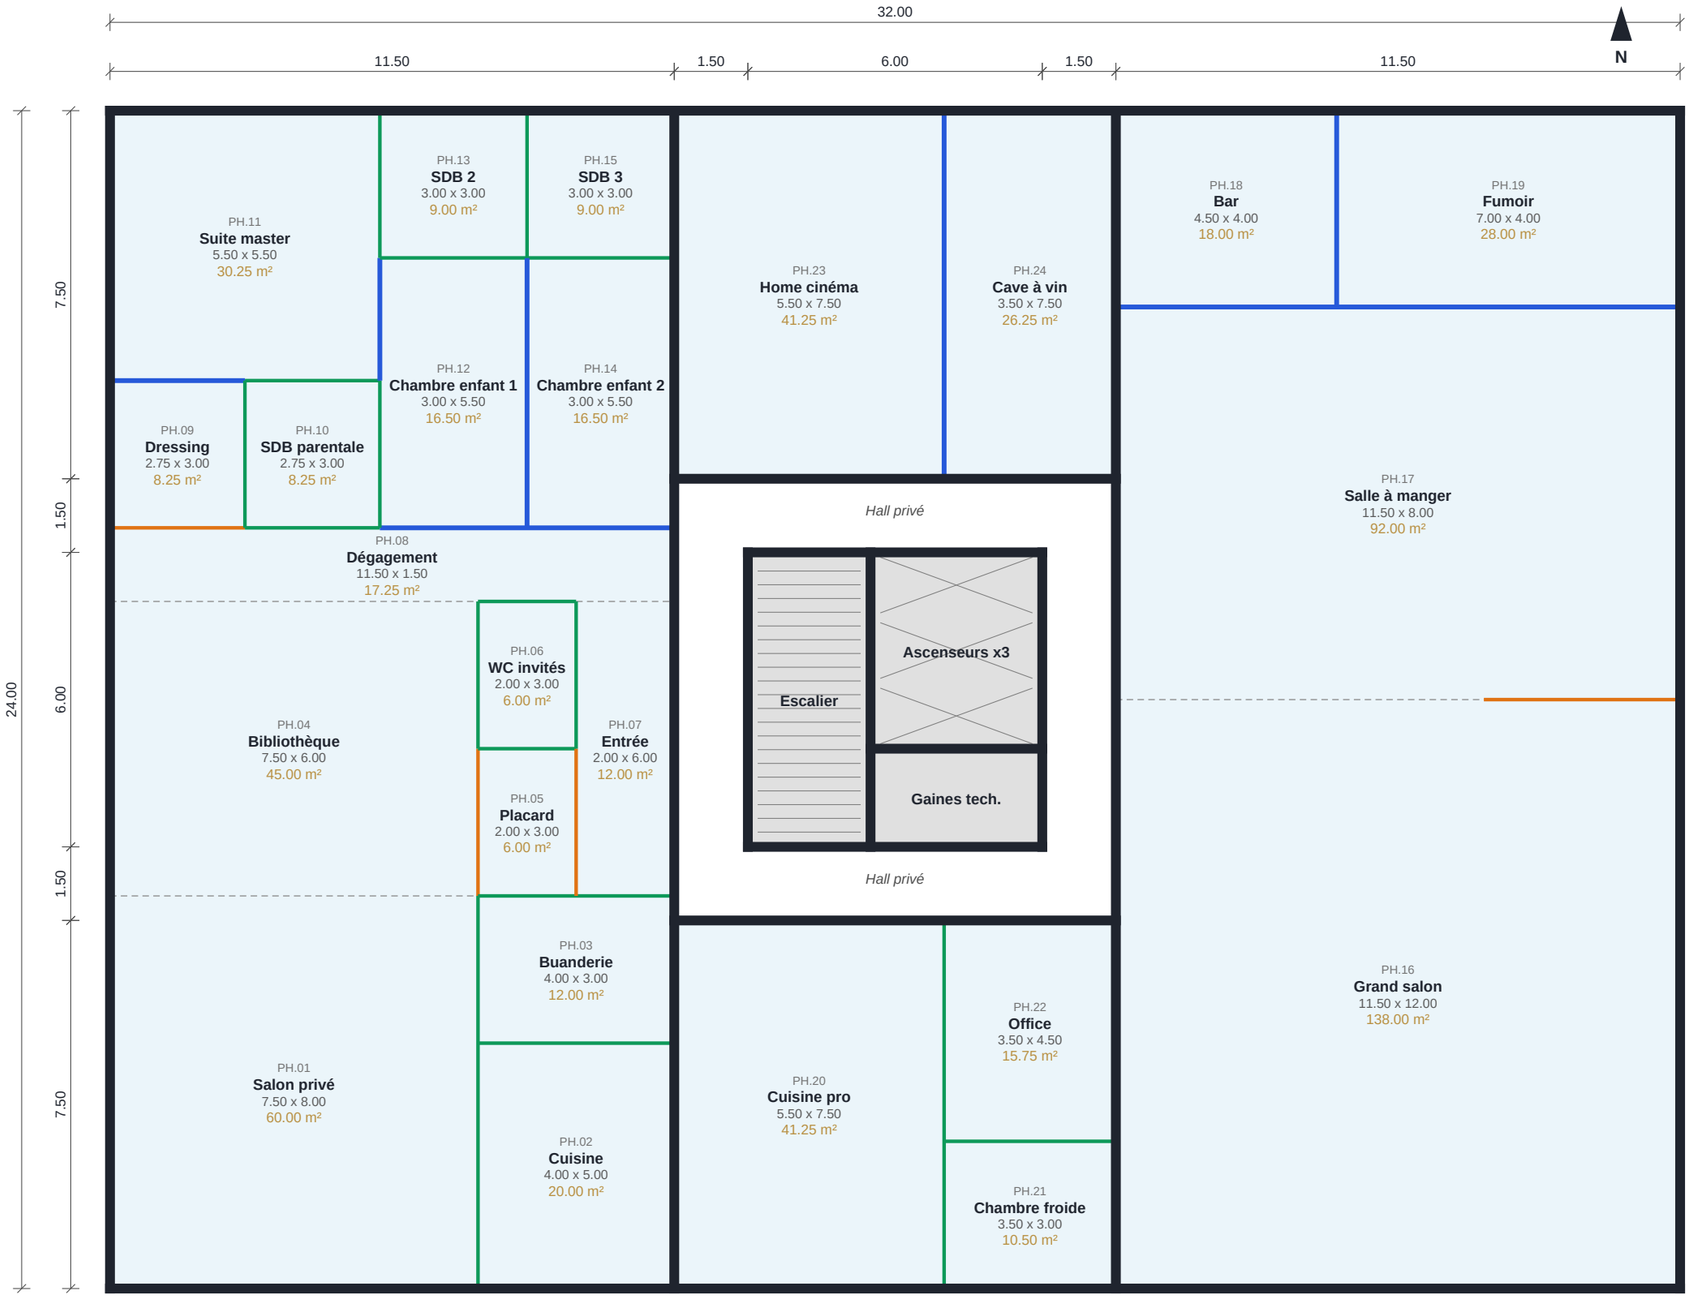

PLAN TEST - PROJET FICTIF

TOUR HORIZON R+40

Résidence grand standing - Dakar

Emprise 32,00 x 24,00 m

R+40

Penthouse

Niveaux concernés	**1**
Hauteur cloisons (dalle/plafond)	**3.20 m**
Échelle	**1/125 (format A3)**
Date	**29/10/2026**
Planche	**6/6**

0 m — 5 m

LÉGENDE

- Voile / mur béton 20 cm
- Cloison 72/48 - 1 BA13 std chaque face
- Cloison 72/48 - BA13 hydro H1 (pièces humides)
- Cloison 98/48 - 2 BA13 chaque face + laine 45 mm
- Limite de zone (sans cloison)

NOTES

- Cotes en mètres, nu intérieur fini.
- Étiquette : code / pièce / dimensions / surface.
- Ouvertures (portes) non représentées.
- Cloisons BA13 = repérage couleur.
- Pièces humides : plaques hydro H1.
- Plan fictif destiné aux tests IA.

UniC Plaquiste - Dakar

ANNEXE - CORRIGÉ MÉTRÉ (à retirer avant test IA)

Surfaces = dimensions intérieures. Cloisons : linéaire mesuré à l'axe, surface = linéaire x hauteur, sans déduction des portes. Voiles béton exclus.

RDC - Rez-de-chaussée - Accueil, loge, commerces

Code	Lot	Pièce	Dimensions (m)	Surface m²
Noyau.01	Noyau	Escalier	2.50 x 6.00	15.00
Noyau.02	Noyau	Ascenseurs x3	3.50 x 4.00	14.00
Noyau.03	Noyau	Gaines tech.	3.50 x 2.00	7.00
COM1.01	COM1	Commerce	8.50 x 12.00	102.00
COM1.02	COM1	Réserve	3.00 x 9.00	27.00
COM1.03	COM1	Sanitaire	3.00 x 3.00	9.00
COM2.01	COM2	Commerce	8.50 x 12.00	102.00
COM2.02	COM2	Réserve	3.00 x 9.00	27.00
COM2.03	COM2	Sanitaire	3.00 x 3.00	9.00
HALL.01	HALL	Loge gardien (accueil)	3.00 x 3.50	10.50
HALL.02	HALL	Salle courrier	3.00 x 3.50	10.50
LG.01	LG	Séjour	4.00 x 4.00	16.00
LG.02	LG	Chambre	3.00 x 4.00	12.00
LG.03	LG	SDB	2.00 x 4.00	8.00
LG.04	LG	Cuisine	2.50 x 3.50	8.75
LG.05	LG	Entrée	3.00 x 3.50	10.50
LT.01	LT	Local poubelles	3.50 x 3.50	12.25
SRV.01	SRV	Bureau syndic	5.50 x 6.00	33.00
SRV.02	SRV	Salle de réunion	6.00 x 6.00	36.00
SRV.03	SRV	Sanitaires H	3.00 x 3.00	9.00
SRV.04	SRV	Sanitaires F	3.00 x 3.00	9.00
SRV.05	SRV	Local vélos	5.50 x 6.00	33.00
SRV.06	SRV	Local technique	6.00 x 6.00	36.00
-	Communs	Palier / circulation	hors rectangle	45.00
-	HALL	Hall d'entrée	hors rectangle	46.50
-	SRV	Lobby lounge	hors rectangle	120.00
		TOTAL NIVEAU (hors murs)		**768.00**

Type cloison	Linéaire ml	Haut. m	m² / niveau	Nb niv.	Total m²
Cloison 72/48 - 1 BA13 std chaque face	33.00	4.00	132.00	1	132.00
Cloison 72/48 - BA13 hydro H1 (pièces humides)	47.00	4.00	188.00	1	188.00
Cloison 98/48 - 2 BA13 chaque face + laine 45 mm	44.00	4.00	176.00	1	176.00

R+1 et R+2 - Équipements communs résidents

Code	Lot	Pièce	Dimensions (m)	Surface m²
Noyau.01	Noyau	Escalier	2.50 x 6.00	15.00
Noyau.02	Noyau	Ascenseurs x3	3.50 x 4.00	14.00
Noyau.03	Noyau	Gaines tech.	3.50 x 2.00	7.00
SPORT.01	SPORT	Salle de sport	11.50 x 14.00	161.00
SPORT.02	SPORT	Vestiaire H	5.75 x 5.00	28.75
SPORT.03	SPORT	Vestiaire F	5.75 x 5.00	28.75

Code	Lot	Pièce	Dimensions (m)	Surface m²
SPORT.04	SPORT	Hammam	4.00 x 5.00	20.00
SPORT.05	SPORT	Sauna	3.00 x 5.00	15.00
SPORT.06	SPORT	Salle de massage	4.50 x 5.00	22.50
BUS.01	BUS	Coworking	5.50 x 7.50	41.25
BUS.02	BUS	Box visio 1	3.50 x 3.75	13.12
BUS.03	BUS	Box visio 2	3.50 x 3.75	13.12
CIN.01	CIN	Régie	2.50 x 2.50	6.25
CIN.02	CIN	Foyer cinéma	6.50 x 2.50	16.25
CIN.03	CIN	Cinéma privé	9.00 x 5.00	45.00
EVT.01	EVT	Salle polyvalente	11.50 x 12.00	138.00
EVT.02	EVT	Office traiteur	4.50 x 4.00	18.00
EVT.03	EVT	Sanitaires	4.50 x 4.00	18.00
EVT.04	EVT	Rangement	4.50 x 4.00	18.00
EVT.05	EVT	Espace enfants	7.00 x 12.00	84.00
-	Communs	Palier / circulation	hors rectangle	45.00
		TOTAL NIVEAU (hors murs)		**768.00**

Type cloison	Linéaire ml	Haut. m	m² / niveau	Nb niv.	Total m²
Cloison 72/48 - 1 BA13 std chaque face	4.00	3.50	14.00	2	28.00
Cloison 72/48 - BA13 hydro H1 (pièces humides)	59.50	3.50	208.25	2	416.50
Cloison 98/48 - 2 BA13 chaque face + laine 45 mm	29.50	3.50	103.25	2	206.50

R+3 à R+35 - Étage courant type 1 - 2 x F5 + 2 x F2

Code	Lot	Pièce	Dimensions (m)	Surface m²
Noyau.01	Noyau	Escalier	2.50 x 6.00	15.00
Noyau.02	Noyau	Ascenseurs x3	3.50 x 4.00	14.00
Noyau.03	Noyau	Gaines tech.	3.50 x 2.00	7.00
A.01	A	Séjour	7.50 x 8.00	60.00
A.02	A	Cuisine	4.00 x 5.00	20.00
A.03	A	Buanderie	4.00 x 3.00	12.00
A.04	A	Salle à manger	7.50 x 6.00	45.00
A.05	A	Placard	2.00 x 3.00	6.00
A.06	A	WC invités	2.00 x 3.00	6.00
A.07	A	Entrée	2.00 x 6.00	12.00
A.08	A	Dégagement	11.50 x 1.50	17.25
A.09	A	Dressing	2.75 x 3.00	8.25
A.10	A	SDB parentale	2.75 x 3.00	8.25
A.11	A	Chambre parentale	5.50 x 5.50	30.25
A.12	A	Chambre 2	3.00 x 5.50	16.50
A.13	A	SDB 2	3.00 x 3.00	9.00
A.14	A	Chambre 3	3.00 x 5.50	16.50
A.15	A	SDB 3	3.00 x 3.00	9.00
B.01	B	Séjour	7.50 x 8.00	60.00
B.02	B	Cuisine	4.00 x 5.00	20.00
B.03	B	Buanderie	4.00 x 3.00	12.00
B.04	B	Salle à manger	7.50 x 6.00	45.00
B.05	B	Placard	2.00 x 3.00	6.00
B.06	B	WC invités	2.00 x 3.00	6.00

Code	Lot	Pièce	Dimensions (m)	Surface m²
B.07	B	Entrée	2.00 x 6.00	12.00
B.08	B	Dégagement	11.50 x 1.50	17.25
B.09	B	Dressing	2.75 x 3.00	8.25
B.10	B	SDB parentale	2.75 x 3.00	8.25
B.11	B	Chambre parentale	5.50 x 5.50	30.25
B.12	B	Chambre 2	3.00 x 5.50	16.50
B.13	B	SDB 2	3.00 x 3.00	9.00
B.14	B	Chambre 3	3.00 x 5.50	16.50
B.15	B	SDB 3	3.00 x 3.00	9.00
C.01	C	Séjour	5.50 x 5.00	27.50
C.02	C	Chambre	3.50 x 4.50	15.75
C.03	C	SDB	3.50 x 3.00	10.50
C.04	C	Cuisine	3.00 x 2.50	7.50
C.05	C	Entrée	2.50 x 2.50	6.25
D.01	D	Séjour	5.50 x 5.00	27.50
D.02	D	Chambre	3.50 x 4.50	15.75
D.03	D	SDB	3.50 x 3.00	10.50
D.04	D	Cuisine	3.00 x 2.50	7.50
D.05	D	Entrée	2.50 x 2.50	6.25
-	Communs	Palier / circulation	hors rectangle	45.00
		TOTAL NIVEAU (hors murs)		**768.00**

Type cloison	Linéaire ml	Haut. m	m² / niveau	Nb niv.	Total m²
Cloison 72/48 - 1 BA13 std chaque face	17.50	2.80	49.00	33	1617.00
Cloison 72/48 - BA13 hydro H1 (pièces humides)	117.00	2.80	327.60	33	10810.80
Cloison 98/48 - 2 BA13 chaque face + laine 45 mm	42.50	2.80	119.00	33	3927.00

R+36 à R+39 - Étage type 2 - F5 + F4 + F2 + 2 studios

Code	Lot	Pièce	Dimensions (m)	Surface m²
Noyau.01	Noyau	Escalier	2.50 x 6.00	15.00
Noyau.02	Noyau	Ascenseurs x3	3.50 x 4.00	14.00
Noyau.03	Noyau	Gaines tech.	3.50 x 2.00	7.00
A.01	A	Séjour	7.50 x 8.00	60.00
A.02	A	Cuisine	4.00 x 5.00	20.00
A.03	A	Buanderie	4.00 x 3.00	12.00
A.04	A	Salle à manger	7.50 x 6.00	45.00
A.05	A	Placard	2.00 x 3.00	6.00
A.06	A	WC invités	2.00 x 3.00	6.00
A.07	A	Entrée	2.00 x 6.00	12.00
A.08	A	Dégagement	11.50 x 1.50	17.25
A.09	A	Dressing	2.75 x 3.00	8.25
A.10	A	SDB parentale	2.75 x 3.00	8.25
A.11	A	Chambre parentale	5.50 x 5.50	30.25
A.12	A	Chambre 2	3.00 x 5.50	16.50
A.13	A	SDB 2	3.00 x 3.00	9.00
A.14	A	Chambre 3	3.00 x 5.50	16.50
A.15	A	SDB 3	3.00 x 3.00	9.00
E.01	E	Séjour	8.00 x 9.00	72.00

Code	Lot	Pièce	Dimensions (m)	Surface m²
E.02	E	Cuisine	3.50 x 5.50	19.25
E.03	E	Cellier	3.50 x 3.50	12.25
E.04	E	Entrée	3.50 x 6.00	21.00
E.05	E	Bureau / salon TV	8.00 x 6.00	48.00
E.06	E	Dégagement	11.50 x 1.50	17.25
E.07	E	SDB	2.50 x 3.50	8.75
E.08	E	WC	1.50 x 3.50	5.25
E.09	E	Dégag. nuit	1.50 x 3.50	5.25
E.10	E	Dressing	3.00 x 3.00	9.00
E.11	E	SDB parentale	3.00 x 3.00	9.00
E.12	E	Suite parentale	6.00 x 4.50	27.00
E.13	E	Chambre 2	5.50 x 4.00	22.00
D.01	D	Séjour	5.50 x 5.00	27.50
D.02	D	Chambre	3.50 x 4.50	15.75
D.03	D	SDB	3.50 x 3.00	10.50
D.04	D	Cuisine	3.00 x 2.50	7.50
D.05	D	Entrée	2.50 x 2.50	6.25
S1.01	S1	Pièce principale	4.50 x 5.00	22.50
S1.02	S1	Kitchenette	1.75 x 2.50	4.38
S1.03	S1	Entrée	1.25 x 2.50	3.12
S1.04	S1	SDB	1.50 x 2.50	3.75
S2.01	S2	Pièce principale	4.50 x 5.00	22.50
S2.02	S2	Kitchenette	1.75 x 2.50	4.38
S2.03	S2	Entrée	1.25 x 2.50	3.12
S2.04	S2	SDB	1.50 x 2.50	3.75
-	Communs	Palier / circulation	hors rectangle	45.00
		TOTAL NIVEAU (hors murs)		**768.00**

Type cloison	Linéaire ml	Haut. m	m² / niveau	Nb niv.	Total m²
Cloison 72/48 - 1 BA13 std chaque face	31.75	2.80	88.90	4	355.60
Cloison 72/48 - BA13 hydro H1 (pièces humides)	104.50	2.80	292.60	4	1170.40
Cloison 98/48 - 2 BA13 chaque face + laine 45 mm	30.25	2.80	84.70	4	338.80

R+40 - Penthouse

Code	Lot	Pièce	Dimensions (m)	Surface m²
Noyau.01	Noyau	Escalier	2.50 x 6.00	15.00
Noyau.02	Noyau	Ascenseurs x3	3.50 x 4.00	14.00
Noyau.03	Noyau	Gaines tech.	3.50 x 2.00	7.00
PH.01	PH	Salon privé	7.50 x 8.00	60.00
PH.02	PH	Cuisine	4.00 x 5.00	20.00
PH.03	PH	Buanderie	4.00 x 3.00	12.00
PH.04	PH	Bibliothèque	7.50 x 6.00	45.00
PH.05	PH	Placard	2.00 x 3.00	6.00
PH.06	PH	WC invités	2.00 x 3.00	6.00
PH.07	PH	Entrée	2.00 x 6.00	12.00
PH.08	PH	Dégagement	11.50 x 1.50	17.25
PH.09	PH	Dressing	2.75 x 3.00	8.25
PH.10	PH	SDB parentale	2.75 x 3.00	8.25

Code	Lot	Pièce	Dimensions (m)	Surface m²
PH.11	PH	Suite master	5.50 x 5.50	30.25
PH.12	PH	Chambre enfant 1	3.00 x 5.50	16.50
PH.13	PH	SDB 2	3.00 x 3.00	9.00
PH.14	PH	Chambre enfant 2	3.00 x 5.50	16.50
PH.15	PH	SDB 3	3.00 x 3.00	9.00
PH.16	PH	Grand salon	11.50 x 12.00	138.00
PH.17	PH	Salle à manger	11.50 x 8.00	92.00
PH.18	PH	Bar	4.50 x 4.00	18.00
PH.19	PH	Fumoir	7.00 x 4.00	28.00
PH.20	PH	Cuisine pro	5.50 x 7.50	41.25
PH.21	PH	Chambre froide	3.50 x 3.00	10.50
PH.22	PH	Office	3.50 x 4.50	15.75
PH.23	PH	Home cinéma	5.50 x 7.50	41.25
PH.24	PH	Cave à vin	3.50 x 7.50	26.25
-	PH	Hall privé	hors rectangle	45.00
		TOTAL NIVEAU (hors murs)		**768.00**

Type cloison	Linéaire ml	Haut. m	m² / niveau	Nb niv.	Total m²
Cloison 72/48 - 1 BA13 std chaque face	12.75	3.20	40.80	1	40.80
Cloison 72/48 - BA13 hydro H1 (pièces humides)	60.50	3.20	193.60	1	193.60
Cloison 98/48 - 2 BA13 chaque face + laine 45 mm	39.75	3.20	127.20	1	127.20

RÉCAPITULATIF TOUR (41 niveaux)

Type cloison	Linéaire total ml	Surface totale m²
Cloison 72/48 - 1 BA13 std chaque face	758.25	2 173.40
Cloison 72/48 - BA13 hydro H1 (pièces humides)	4 505.50	12 779.30
Cloison 98/48 - 2 BA13 chaque face + laine 45 mm	1 666.25	4 775.50
TOTAL	**6 930.00**	**19 728.20**